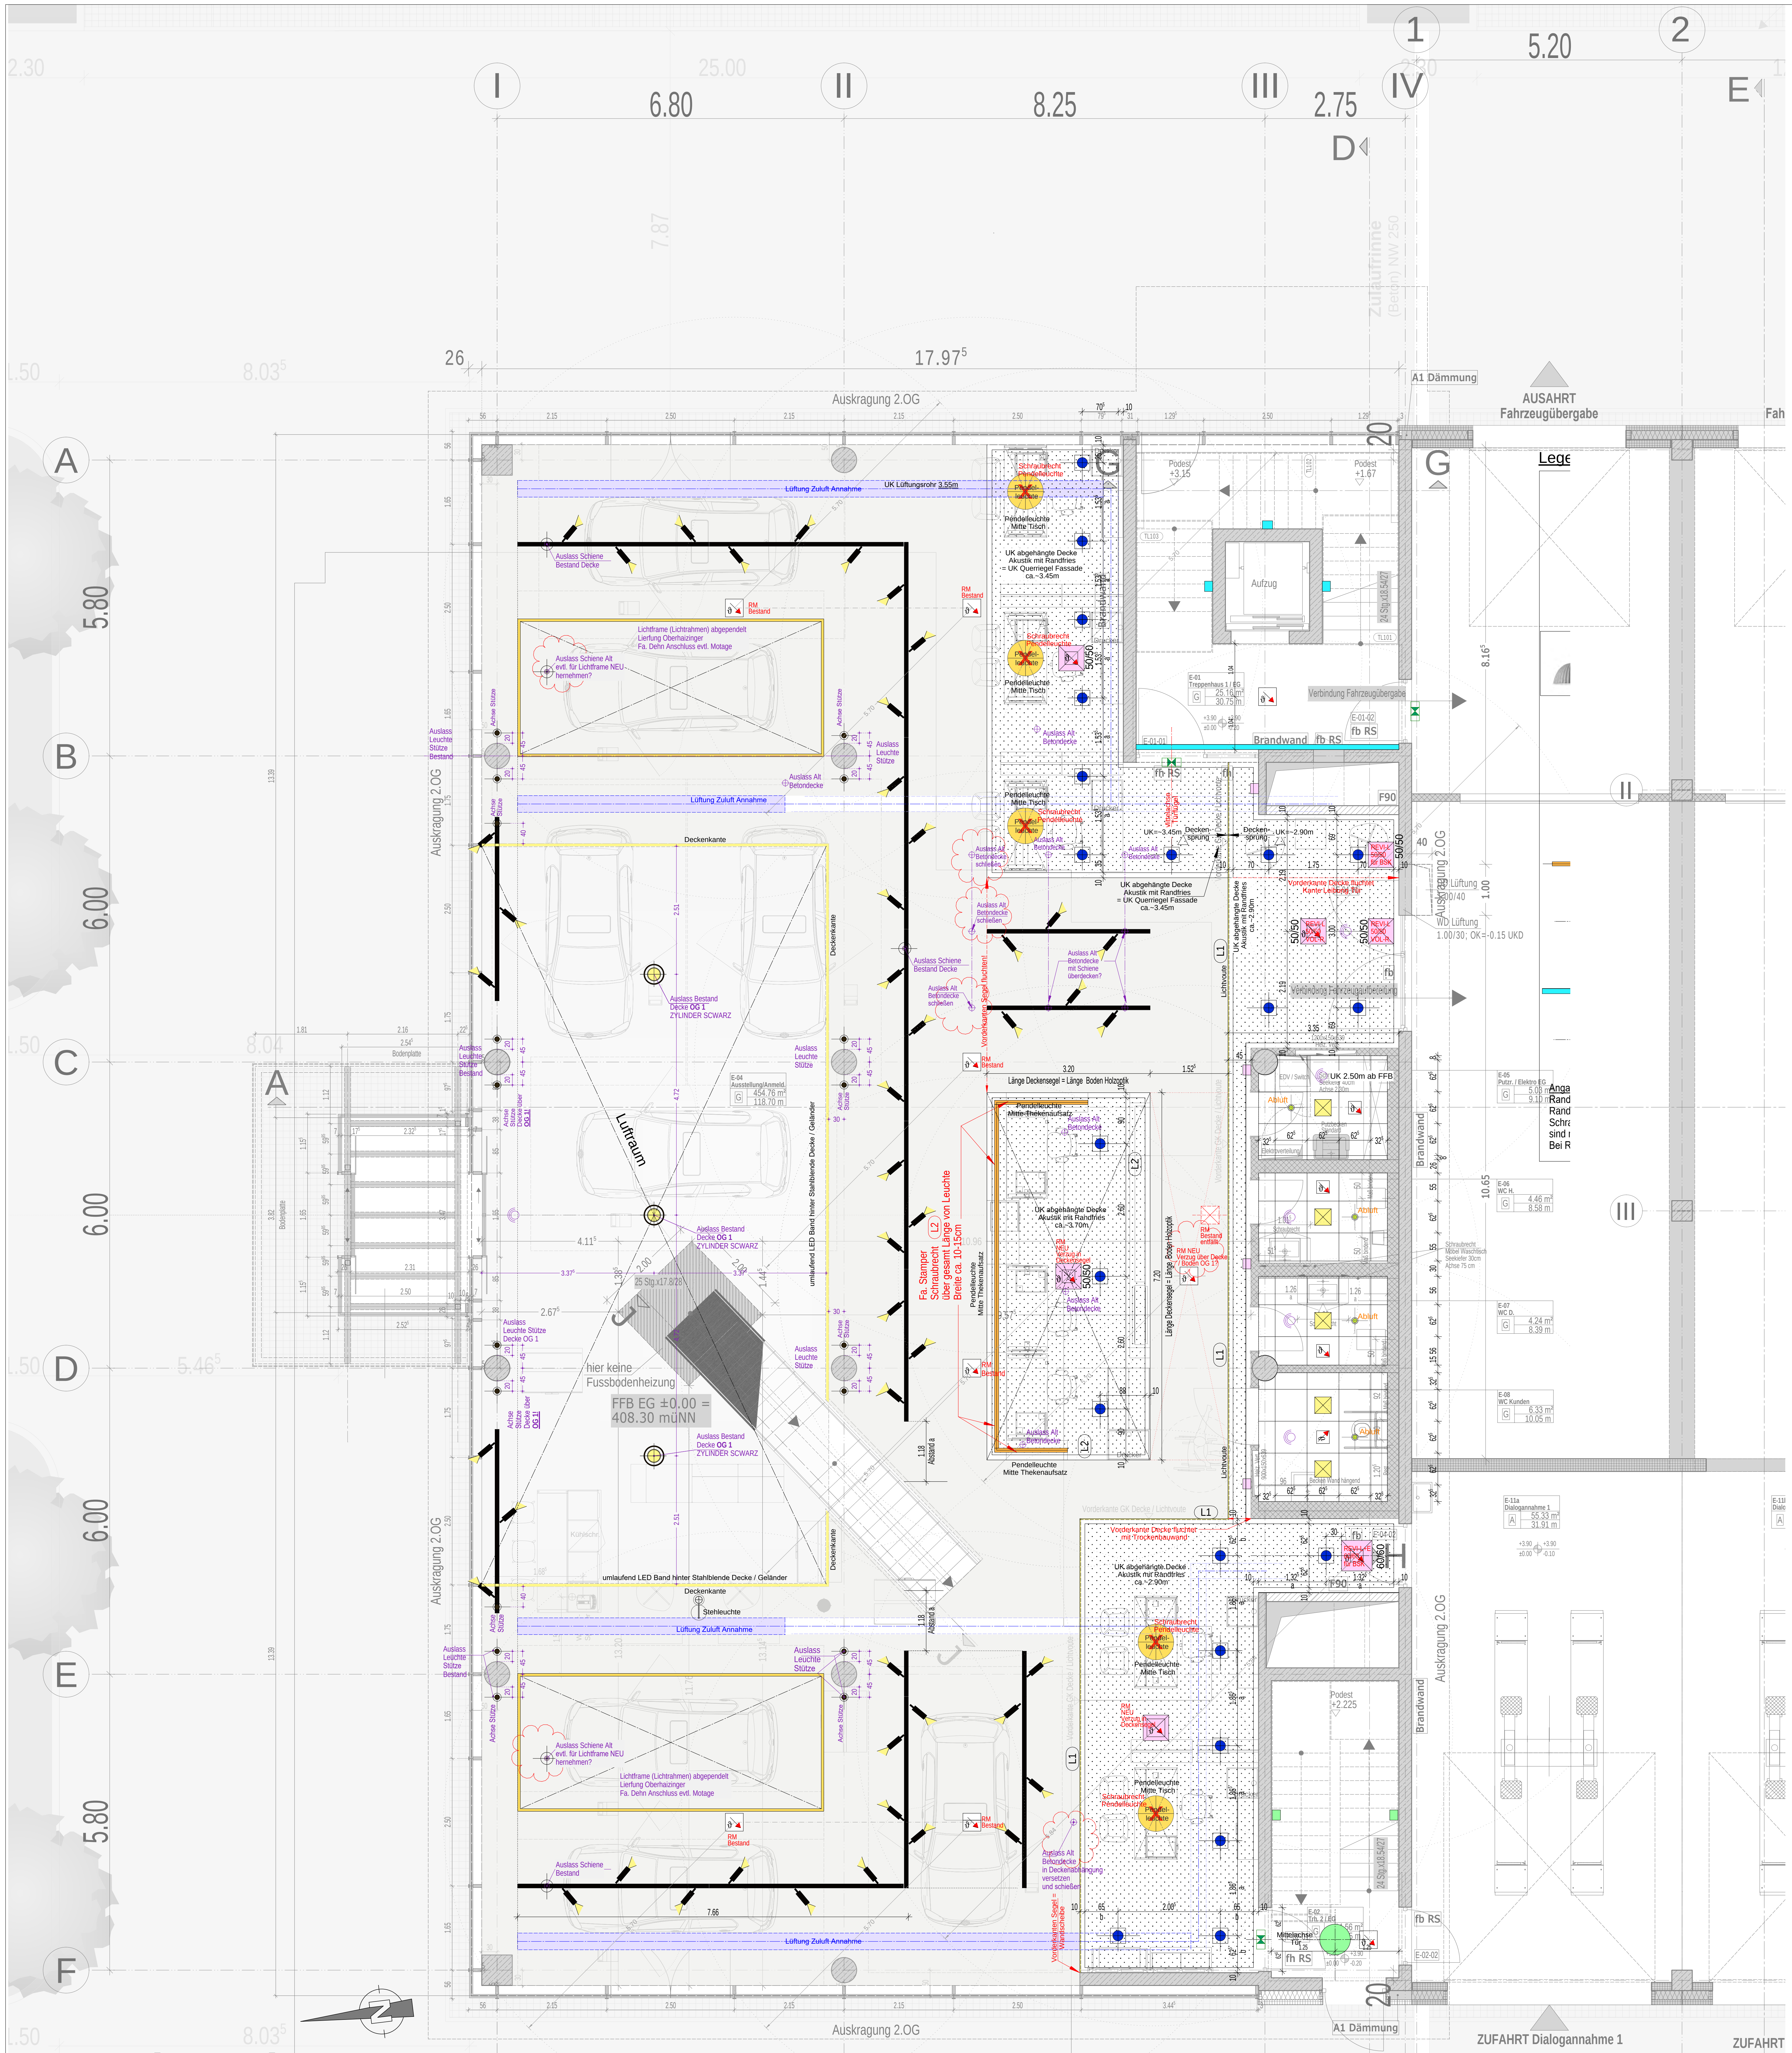

I
II
III
IV
1
2
A
B
C
D
E
F
6.80
8.25
2.75
5.20
5.80
6.00
6.00
6.00
5.80
26
17.97⁵
Auskragung 2.OG
AUSAHRT Fahrzeugübergabe
A1 Dämmung
Luftraum
Aufzug
Lüftung Zuluft Annahme
Deckenkante
hier keine Fussbodenheizung
FFB EG ±0.00 = 408.30 müNN
Brandwand
ZUFAHRT Dialogannahme 1
ZUFAHRT
Pendelleuchte Mitte Tisch
UK abgehängte Decke Akustik mit Randfries
Länge Deckensegel = Länge Boden Holzoptik
Fa. Stamper Schraubrecht über gesamt Länge von Leuchte Breite ca. 10-15cm
umlaufend LED Band hinter Stahlblende Decke / Geländer

# Erdgeschoss

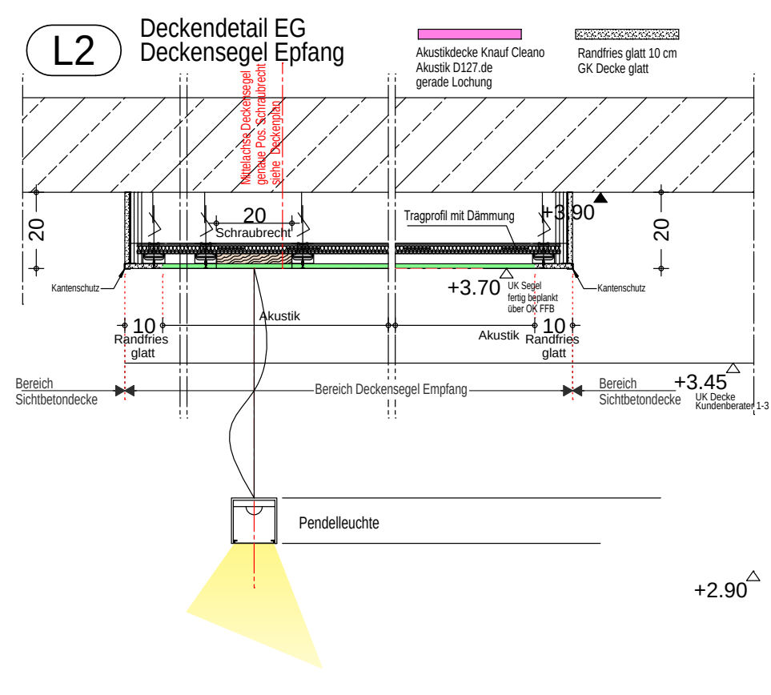

L2
Deckendetail EG
Deckensegel Epfang
Akustikdecke Knauf Cleano Akustik D127.de gerade Lochung
Randfries glatt 10 cm GK Decke glatt
Mittelachse Deckensegel genaue Pos. Schraubrecht siehe Deckenplan
20
Schraubrecht
Tragprofil mit Dämmung
+3.90
+3.70
UK Segel fertig beplankt über OK FFB
Kantenschutz
Akustik
10
Randfries glatt
Bereich Sichtbetondecke
Bereich Deckensegel Empfang
+3.45
UK Decke Kundenberater 1-3
Pendelleuchte
+2.90

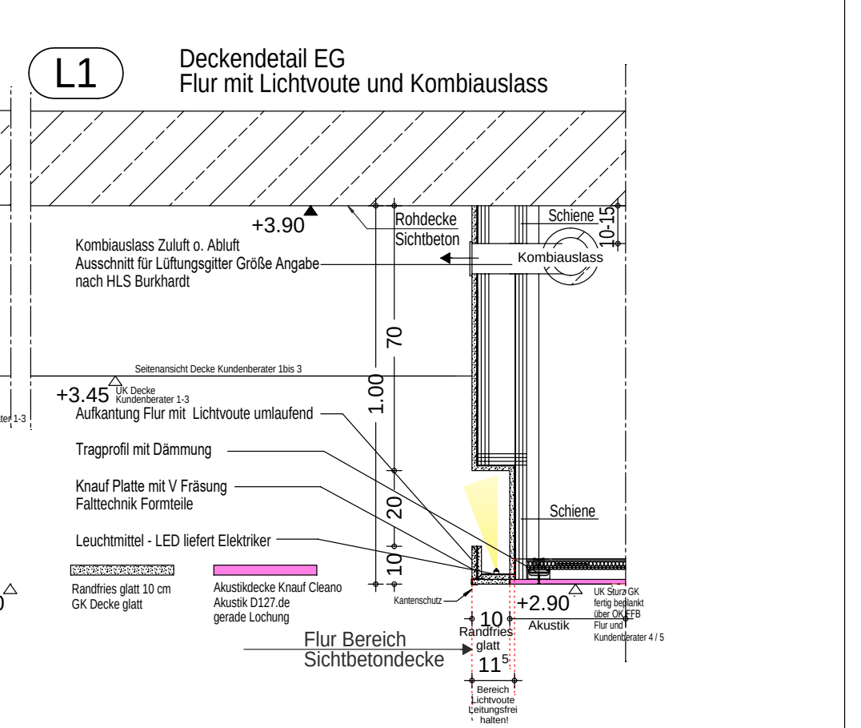

L1
Deckendetail EG
Flur mit Lichtvoute und Kombiauslass
+3.90
Rohdecke Sichtbeton
Schiene
10-15
Kombiauslass
Kombiauslass Zuluft o. Abluft Ausschnitt für Lüftungsgitter Größe Angabe nach HLS Burkhardt
70
1.00
20
10
Seitenansicht Decke Kundenberater 1bis 3
+3.45
UK Decke Kundenberater 1-3
Aufkantung Flur mit Lichtvoute umlaufend
Tragprofil mit Dämmung
Knauf Platte mit V Fräsung Falttechnik Formteile
Leuchtmittel - LED liefert Elektriker
Randfries glatt 10 cm GK Decke glatt
Akustikdecke Knauf Cleano Akustik D127.de gerade Lochung
Kantenschutz
+2.90
UK Sturz GK fertig beplankt über OK FFB Flur und Kundenberater 4 / 5
Akustik
Randfries glatt
11⁵
Bereich Lichtvoute Leitungsfrei halten!
Flur Bereich Sichtbetondecke

## Legende Decke

| | |
|---|---|
| ⌖ | Aufbauleuchte an Stütze<br>Brumberg TRAXX Maxi d=8,5cm<br>Pos. 25.14.87+90 |
| ☒ | (DA) RZB Sidlelite ECO 324 x324mm<br>Pos. 25.14.207 |
| ☒ | (EA) RIDI FPL4 weiß<br>für Raster 62,5 x62,5cm<br>Pos. 25.14.139 |
| ◎ | Pendelleuchten<br>Hallenreflektorleuchten d= 262mm ca.75 cm abgependelt<br>Zylindergehäuse d= 40 cm x Länge 80 cmSchwarz mit Lüftungsschlitzen<br>(Kaminwirkung mit Wärmeentwicklung) bauseits über Metallbauer? |
| Pendel-leuchte | Pendelleuchte<br>Muuto Under the Bell<br>H: 46 Ø: 82 mit 500cm Netzkabel, Grey<br>Lieferumfang Oberhaizinger<br>Fa. Dehn nur Auslass / evtl. Montage |
| X | Fa. Stamper<br>Schraubrecht Maße im Plan an Leuchte<br>in Anlehung an L7 |
| ⊕ | Deckeneinbau mit Randfries in Akustikdecke<br>XAL MITA Cirkle 200 opal im Flur Flur<br>über APL Empfang u.Kundenberater mit Reflector<br>DA D=200mm<br>Einbautiefe ca. 62mm<br>Ausschnitt nach Angabe Dehn<br>Pos. 25.14.116 |
| ▬ | Pendelleuchte Matric System G5 \| 81mm Suspended<br>mit Ablendraster / Microprismatic<br>über Eck 90° Corner (2 Stück)<br>PC-Arbeitsplatz tauglich!<br>Farbe WEISS |
| ⊕ | Deckenleuchte / Wandleuchte Aufbau<br>Treppenhaus 1<br>Basic Deco Y3/X3 Schwarz<br>Pos. 25.14.138 |
| ▬ | Wand / Deckenleuchte Lichtkanal<br>Schwarz Aufbau Treppenhaus<br>Lightnet Matrix Abdeckung Opal |
| ⊕ | Deckenleuchte / Wandleuchte Aufbau<br>Treppenhaus 2<br>Flat Polymero Kreis Slim<br>Pos. 25.14.136 |
| | Stromschienen mit Strahler / d=10 bis 20cm/ H= ca. 25 cm<br>direkt unter Betondecke montiert<br>Schwarz UK Schiene ca. ......Festlegung mit BH<br>(Erco / Brumberg / XAL....) |
| ◻ | Wandleuchte Aufbau Würfel<br>118x118x118mm in Schwarz<br>Brumberg Dulvia LED<br>Pos. 25.14.205 |
| L 1 bis L 7 | indirektes Licht in GK Decke Voute<br>LED-Profilelement Art.Nr. 10.0002 DSL Flex<br>(gebogene Ausführung) Profiltechnik GmbH Mühlhausen<br>12,5 / 2,0 m / inkl. Grundierung vom Trockenbauer<br>POWER Led Strip mit Trafo, 2700K vom Elektriker |
| ☒ | Revisionsdeckel (Abgehängte Decke muss<br>in diesem Bereich abnehmbar sein)<br>Größe: 600x600mm wenn nicht anders angegeben |
| ⧓ | Notleuchte Dauerlicht Piktogramm Fluchtweg<br>Angabe Brandschutzkonzept |
| ϑ | Rauchmelder (Deckenaufbau)<br>In Gruppen evtl,. zusammen gefasst. |
| ϑ XX/XX | Rauchmelder (Deckenaufbau) Decke abgehängt<br>u. auf Rohdecke in Hohlraum , Rev. Offnung<br>Größe Revi in Zeichnung |
| ◎ | Bewegungsmelder für Raumlicht |
| Lüftung Zuluft Annahme | Düsenrohr Ventiduct Rohr Belüftungssystem Zuluft<br>Wickelfalzrohr mit Düsen d= 315 / d (aussen)= 327mm |
| Zuluft<br>Abluft | Leitungen in GK Decke Lüftung |
| Zuluft Abluft | Drallauslass Abluft und Zuluft in abgehängten GK Decken |
| Zuluft Abluft | Lüftungsauslässe - Schlitzdurchlass quer liegend<br>in senkrechter Abkofferung Trockenbau |
| ⊕ Abluft | Abluft Tellerventil Decke WC / Nebenräume |

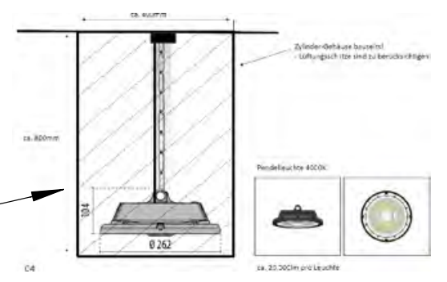

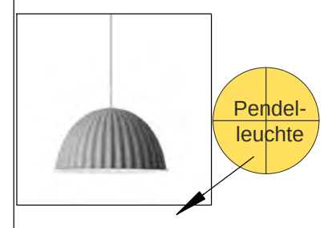

Angaben für Trockenbau:
Randfries um Drallauslässe und Leuchten nur 6cm!
Randfriese Allgemein Segel ca. 10 cm lt. Angaben Plan
Schraubrechte Pendelleuchten
sind mit rotem Kreuz gekennzeichnet.
Bei Rückfragen bitte anrufen! X

| | |
|---|---|
| ⁘ | GK Decke (weiss) Akustik<br>gerade Lochung |
| ▭ | Sichtbetondecke roh |

Deckenplan ERDGESCHOSS

| Plannummer: | Index | Planinhalt: | Planstand vom: |
|---|---|---|---|
| 3024C_04 - 7002 | g | Deckenplan ERDGESCHOSS | 17.12.2025 |

Projekt:
Errichtung eines Autohauses
mit Verwaltung und Werkstatt

Maßstab: 1:50
Gez: KS/MH

Bauherr:
Michael Fleischmann Immobiliengesellschaft mbH
Maria-Hilf-Straße 74
92334 Berching

Erstelldatum: 15.07.2024
Flurnummer: 546/1
Gemarkung: Wappersdorf

Alle Maße sind im Plan und an der Baustelle unter Haftung des Unternehmers zu prüfen.
Alle statischen Werte sind unter Verantwortung und auf Kosten des Unternehmers zu erbringen,
soweit nicht vom Statiker erstellt.

Höhenlage ± 0,00: 408.30 müNN

SÄMTLICHE HÖHEN AB FERTIGFUSSBODEN

| | |
|---|---|
| DD | Deckendurchbruch |
| FDB | Fussbodendurchbruch |
| WD | Wanddurchbruch |
| WS | Wandschlitz |
| OKR | Oberkante Rohboden |
| OKF | Oberkante Fertigboden |
| HKN | Heizkörpernische |
| BRH | Brüstungshöhe ab OKF |
| D 1 | Details mit separaten Deckblättern |
| TR1 | Trockenbaudetails |
| L 1 | Deckendetails ( abgehängte Decken) |
| DF Wand | Dehnungsfuge Wand |
| DF Boden | Dehnungsfuge Boden |
| FL 6 | Fallleitungen (Abwasser) |
| ▨ | Bewehrter Beton |
| ▨ | Mauerwerk |
| ▦ | STB. Fertigteile |
| ▩ | Trockenbauständerwand |
| ▭ | .... |
| ▭ | .... |

Änderungsindex:

| | | | |
|---|---|---|---|
| a | 25.07.2024 | MH | Auslasspunkt zwischen Achse I-II / B entfernt |
| b | 06.08.2024 | MH | Putzraum: Tür verschoben, Elektroverteiler ergänzt, Windfang nach Aussen verschoben |
| c | 17.09.2024 | KS | Beleuchtung aufgrund der Lichtberechnung angepasst |
| d | 16.01.2025 | KS | Segel Arbeitsplätze vermasst und Schraubrechte angepasst, Wartebereich Deckensegel vermasst |
| e | 12.03.2025 | MH | WCs + Putzraum/Elektro EG werden als Rasterdecken ausgeführt |
| f | 15.10.2025 | KS | Deckenplan dem neuen Grundriss angepasst |
| g | 17.12.2025 | MH | REVI-Öffnungen Lüftung gem. Angaben Frau Rohrmüller ergänzt |

**Achtung an Trockenbauer und Elektriker Montage und Einbauten in Akustik-Plattendecke:**
Abstand Achse der UK CD Profile max. 333 mm
Für Montage Aufbaulauchten: Schraubrecht zw. der Unterkonstruktion
mit Lastabtragung an Rohdecke vom Trockenabauer
Für Montage der Einbauleuchten: Lastabtragung Einbauleuchte
durch Einbaurahmen für GK Decken,
evtl. Rükbefestigung an Rohdecke durch Elektriker!

Anmerkungen, Änderungen, Fragen

**Lastangaben für Abgehängte Akustik-Plattendecken:**
**Zulässiges Gewicht je Befestigungspunkt in kg**
Befestigung an der Beplankung 0,5 kg
Befestigung an der Unterkonstruktion 3,0 kg

ACHTUNG !!!
Beim Einbau der Trockenbauwände ist eine Durchbiegung
der Decke bis zu 2 cm zu berücksichtigen!

Alle Angaben im Plan zu Heizung, Elektro, EDV, Sanitär, Kühlung,
Abluft- und Zuluft, dienen als „optischer Endauslassplan".
Diese Planung ersetzt nicht die technische Projektierung
der einzelnen techn. Gewerke Heizung, Lüftung, Sanitär, und Elektro,
sowie Brandschutz und Schallschutz.

Alle Höhenangaben sind Fertigmaße ab /über +/- 0 = Oberkante Fertigfußbodenbelag
des jeweiligen Geschosses ( KG, EG und DG).

Schraubrecht der technischen Gewerke wie z.B für Heizkörper usw.
sind von der auszuführenden Firma oder Fachplaner anzugeben

Planverfasser:
Architekturbüro Theo Nutz GmbH
Nürnberger Straße 48
92318 Neumarkt
09181-6940-0
09181-6940-26
info@nutz-architekten.de

architekturbüro
Theo Nutz

EG | Deckenplan

Allplan 2022