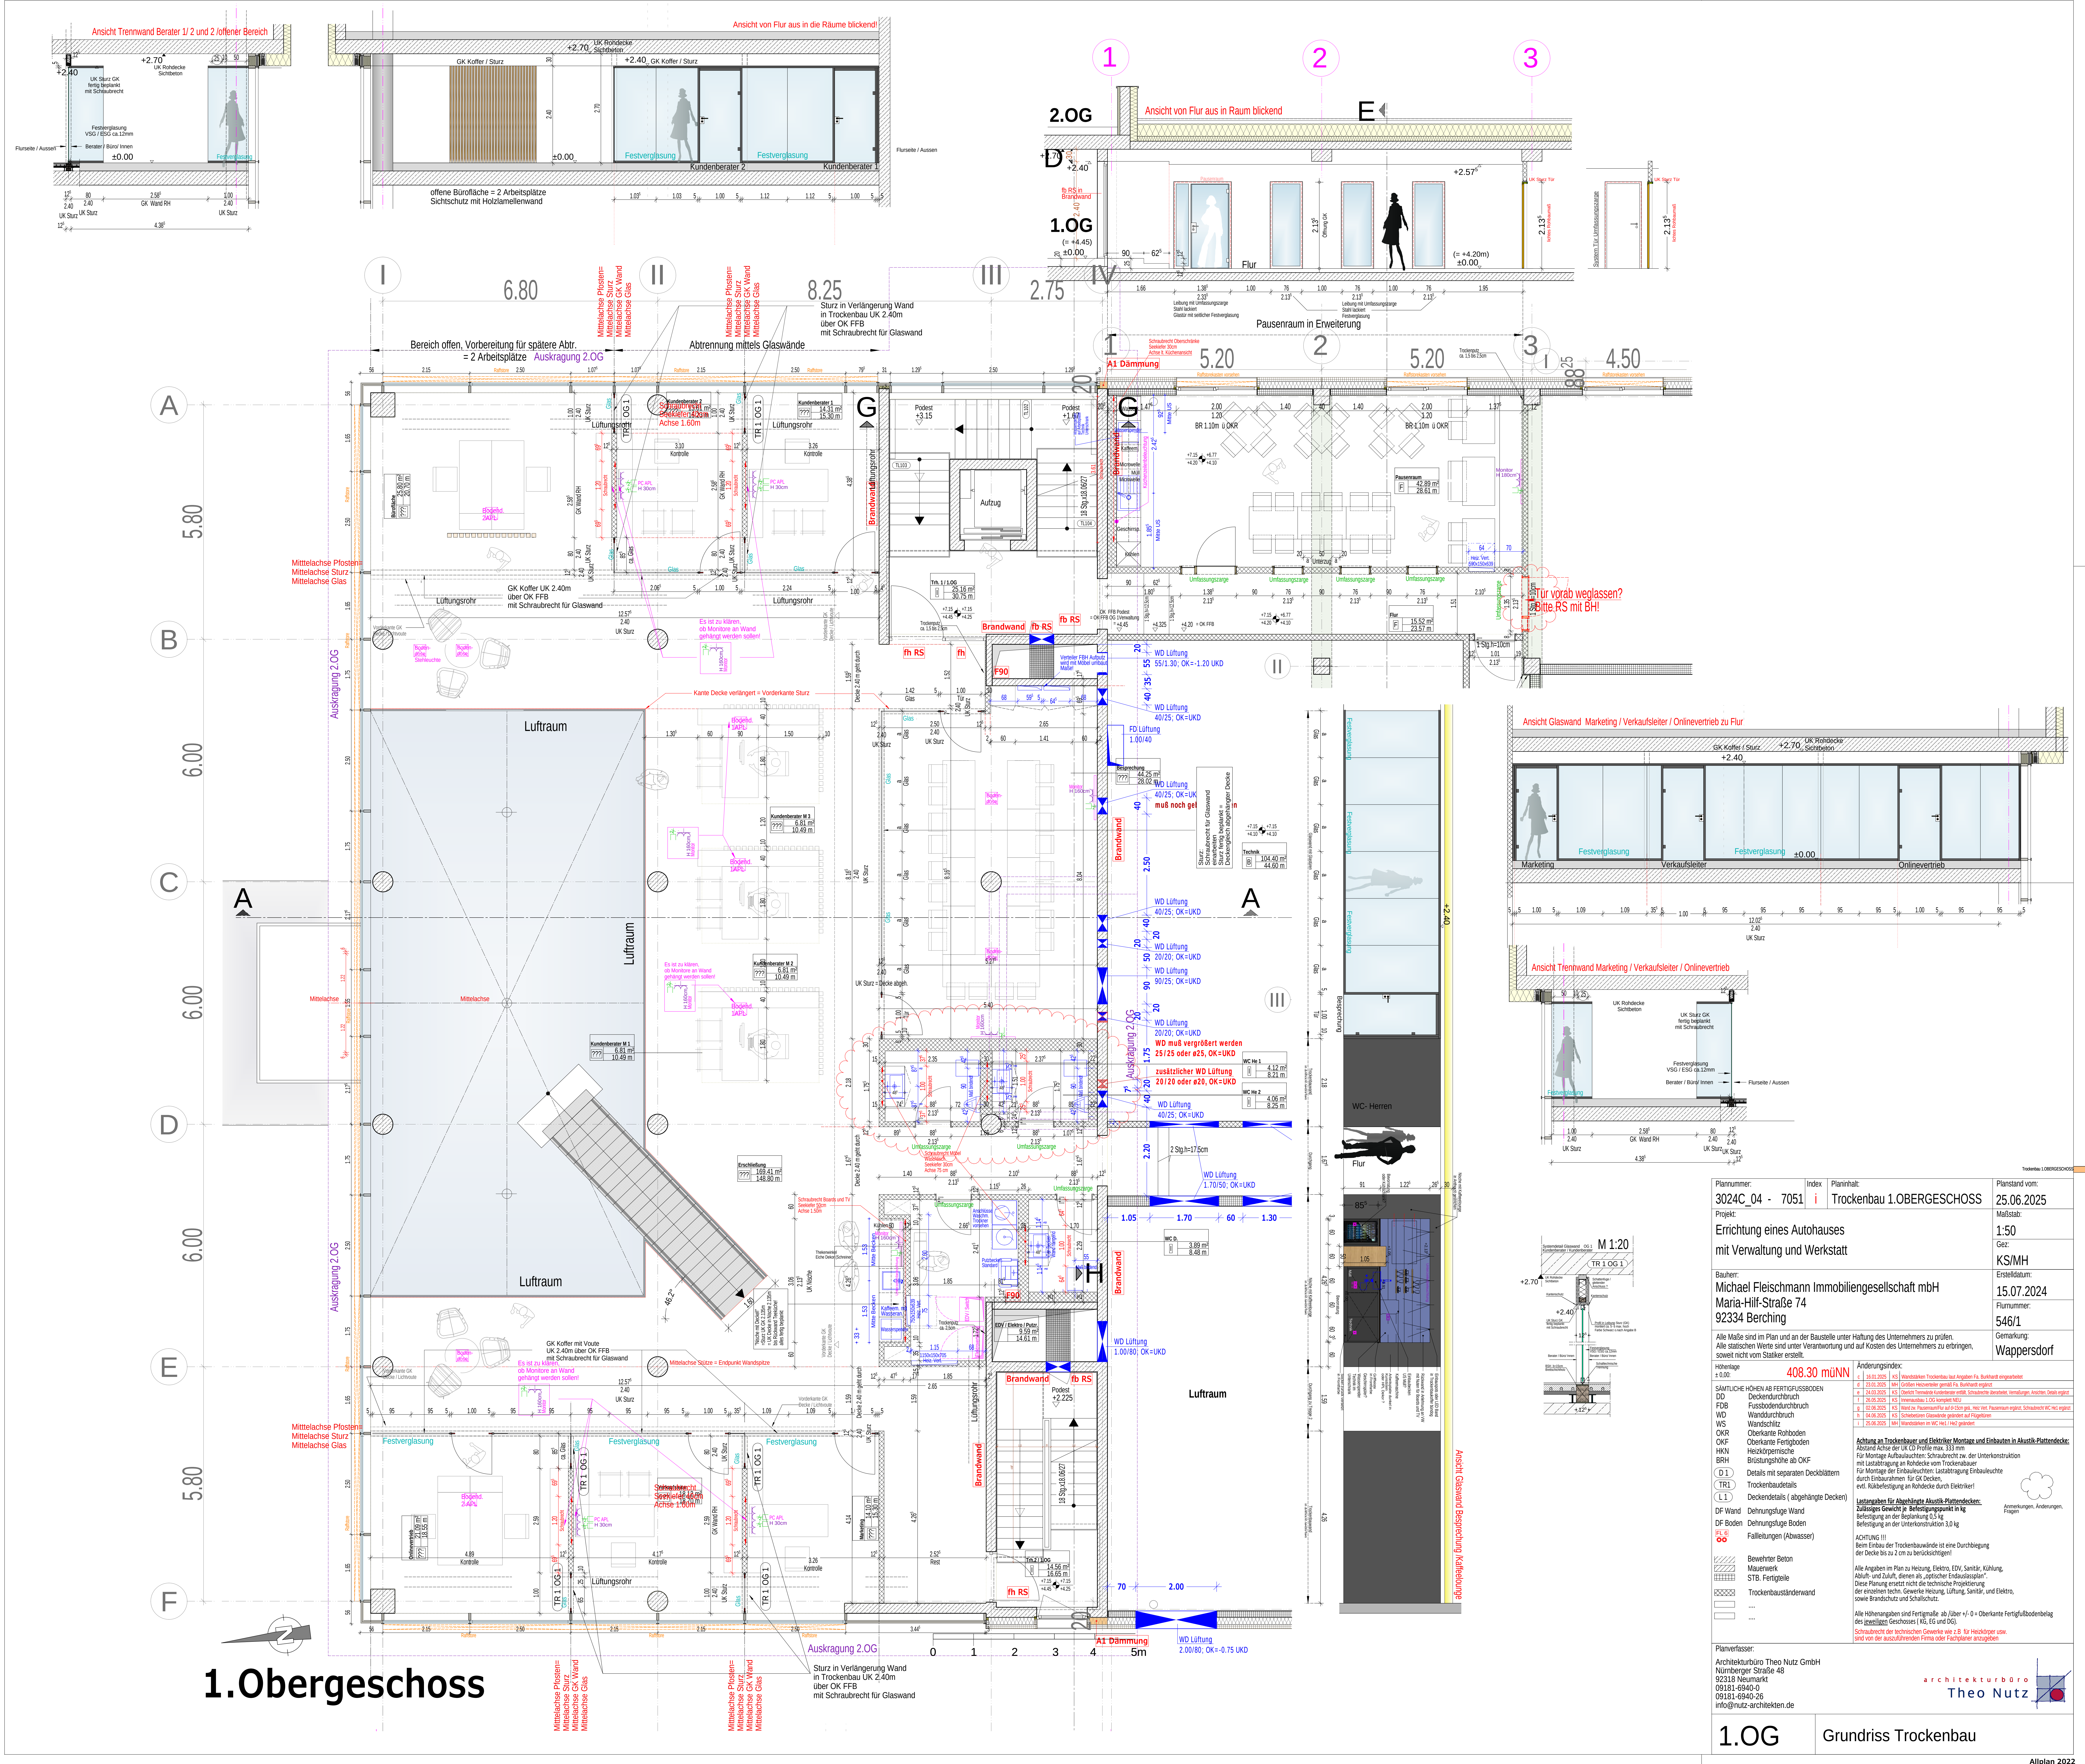
1.Obergeschoss
Ansicht Trennwand Berater 1/ 2 und 2 /offener Bereich
Ansicht von Flur aus in die Räume blickend!
Ansicht von Flur aus in Raum blickend
2.OG
1.OG
Pausenraum in Erweiterung
Ansicht Glaswand Marketing / Verkaufsleiter / Onlinevertrieb zu Flur
Ansicht Trennwand Marketing / Verkaufsleiter / Onlinevertrieb
Ansicht Glaswand Besprechung Kaffeelounge
Bereich offen, Vorbereitung für spätere Abtr. = 2 Arbeitsplätze
Abtrennung mittels Glaswände
Auskragung 2.OG
Luftraum
Brandwand
Aufzug
Pausenraum
Kundenberater 1
Kundenberater 2
Kundenberater M 1
Kundenberater M 2
Kundenberater M 3
Besprechung
Technik
WC He 1
WC He 2
WC D
Marketing
Verkaufsleiter
Onlinevertrieb
WC- Herren
Flur
Festverglasung
Lüftungsrohr
A1 Dämmung
Tür vorab weglassen? Bitte RS mit BH!
WD muß vergrößert werden 25/25 oder ø25, OK=UKD
zusätzlicher WD Lüftung 20/20 oder ø20, OK=UKD
Mittelachse Pfosten= Mittelachse Sturz= Mittelachse GK Wand= Mittelachse Glas
Sturz in Verlängerung Wand in Trockenbau UK 2.40m über OK FFB mit Schraubrecht für Glaswand
6.80
8.25
2.75
5.20
5.20
4.50
5.80
6.00
6.00
6.00
5.80
I
II
III
IV
1
2
3
A
B
C
D
E
F
G
H
M 1:20
0 1 2 3 4 5m

Trockenbau 1.OBERGESCHOSS

Plannummer:	Index	Planinhalt:	Planstand vom:
3024C_04 - 7051	i	Trockenbau 1.OBERGESCHOSS	25.06.2025

Projekt:
Errichtung eines Autohauses
mit Verwaltung und Werkstatt

Maßstab: 1:50

Gez: KS/MH

Bauherr:
Michael Fleischmann Immobiliengesellschaft mbH
Maria-Hilf-Straße 74
92334 Berching

Erstelldatum: 15.07.2024

Flurnummer: 546/1

Gemarkung: Wappersdorf

Alle Maße sind im Plan und an der Baustelle unter Haftung des Unternehmers zu prüfen.
Alle statischen Werte sind unter Verantwortung und auf Kosten des Unternehmers zu erbringen, soweit nicht vom Statiker erstellt.

Höhenlage ± 0,00: 408.30 müNN

Änderungsindex:

c	16.01.2025	KS	Wandstärken Trockenbau laut Angaben Fa. Burkhardt eingearbeitet
d	23.01.2025	MH	Größen Heizverteiler gemäß Fa. Burkhardt ergänzt
e	24.03.2025	KS	Oberlicht Trennwände Kundenberater entfällt, Schraubrechte überarbeitet, Vermaßungen, Ansichten, Details ergänzt
f	26.05.2025	KS	Innenausbau 1.OG komplett NEU
g	02.06.2025	KS	Wand zw. Pausenraum/Flur auf d=15cm geä., Heiz Vert. Pausenraum ergänzt, Schraubrecht WC He1 ergänzt
h	04.06.2025	KS	Schiebetüren Glaswände geändert auf Flügeltüren
i	25.06.2025	MH	Wandstärken im WC He1 / He2 geändert

SÄMTLICHE HÖHEN AB FERTIGFUSSBODEN

DD	Deckendurchbruch
FDB	Fussbodendurchbruch
WD	Wanddurchbruch
WS	Wandschlitz
OKR	Oberkante Rohboden
OKF	Oberkante Fertigboden
HKN	Heizkörpernische
BRH	Brüstungshöhe ab OKF
D 1	Details mit separaten Deckblättern
TR1	Trockenbaudetails
L 1	Deckendetails (abgehängte Decken)
DF Wand	Dehnungsfuge Wand
DF Boden	Dehnungsfuge Boden
FL 6	Fallleitungen (Abwasser)
▨	Bewehrter Beton
▨	Mauerwerk
▦	STB. Fertigteile
▩	Trockenbauständerwand
☐	....
☐	....

Achtung an Trockenbauer und Elektriker Montage und Einbauten in Akustik-Plattendecke:
Abstand Achse der UK CD Profile max. 333 mm
Für Montage Aufbaulauchten: Schraubrecht zw. der Unterkonstruktion
mit Lastabtragung an Rohdecke vom Trockenabauer
Für Montage der Einbauleuchten: Lastabtragung Einbauleuchte
durch Einbaurahmen für GK Decken,
evtl. Rükbefestigung an Rohdecke durch Elektriker!

Lastangaben für Abgehängte Akustik-Plattendecken:
Zulässiges Gewicht je Befestigungspunkt in kg
Befestigung an der Beplankung 0,5 kg
Befestigung an der Unterkonstruktion 3,0 kg

Anmerkungen, Änderungen, Fragen

ACHTUNG !!!
Beim Einbau der Trockenbauwände ist eine Durchbiegung der Decke bis zu 2 cm zu berücksichtigen!

Alle Angaben im Plan zu Heizung, Elektro, EDV, Sanitär, Kühlung, Abluft- und Zuluft, dienen als „optischer Endauslassplan“. Diese Planung ersetzt nicht die technische Projektierung der einzelnen techn. Gewerke Heizung, Lüftung, Sanitär, und Elektro, sowie Brandschutz und Schallschutz.

Alle Höhenangaben sind Fertigmaße ab /über +/- 0 = Oberkante Fertigfußbodenbelag des jeweiligen Geschosses (KG, EG und DG).

Schraubrecht der technischen Gewerke wie z.B für Heizkörper usw. sind von der auszuführenden Firma oder Fachplaner anzugeben

Planverfasser:
Architekturbüro Theo Nutz GmbH
Nürnberger Straße 48
92318 Neumarkt
09181-6940-0
09181-6940-26
info@nutz-architekten.de

architekturbüro
Theo Nutz

1.OG Grundriss Trockenbau

Allplan 2022