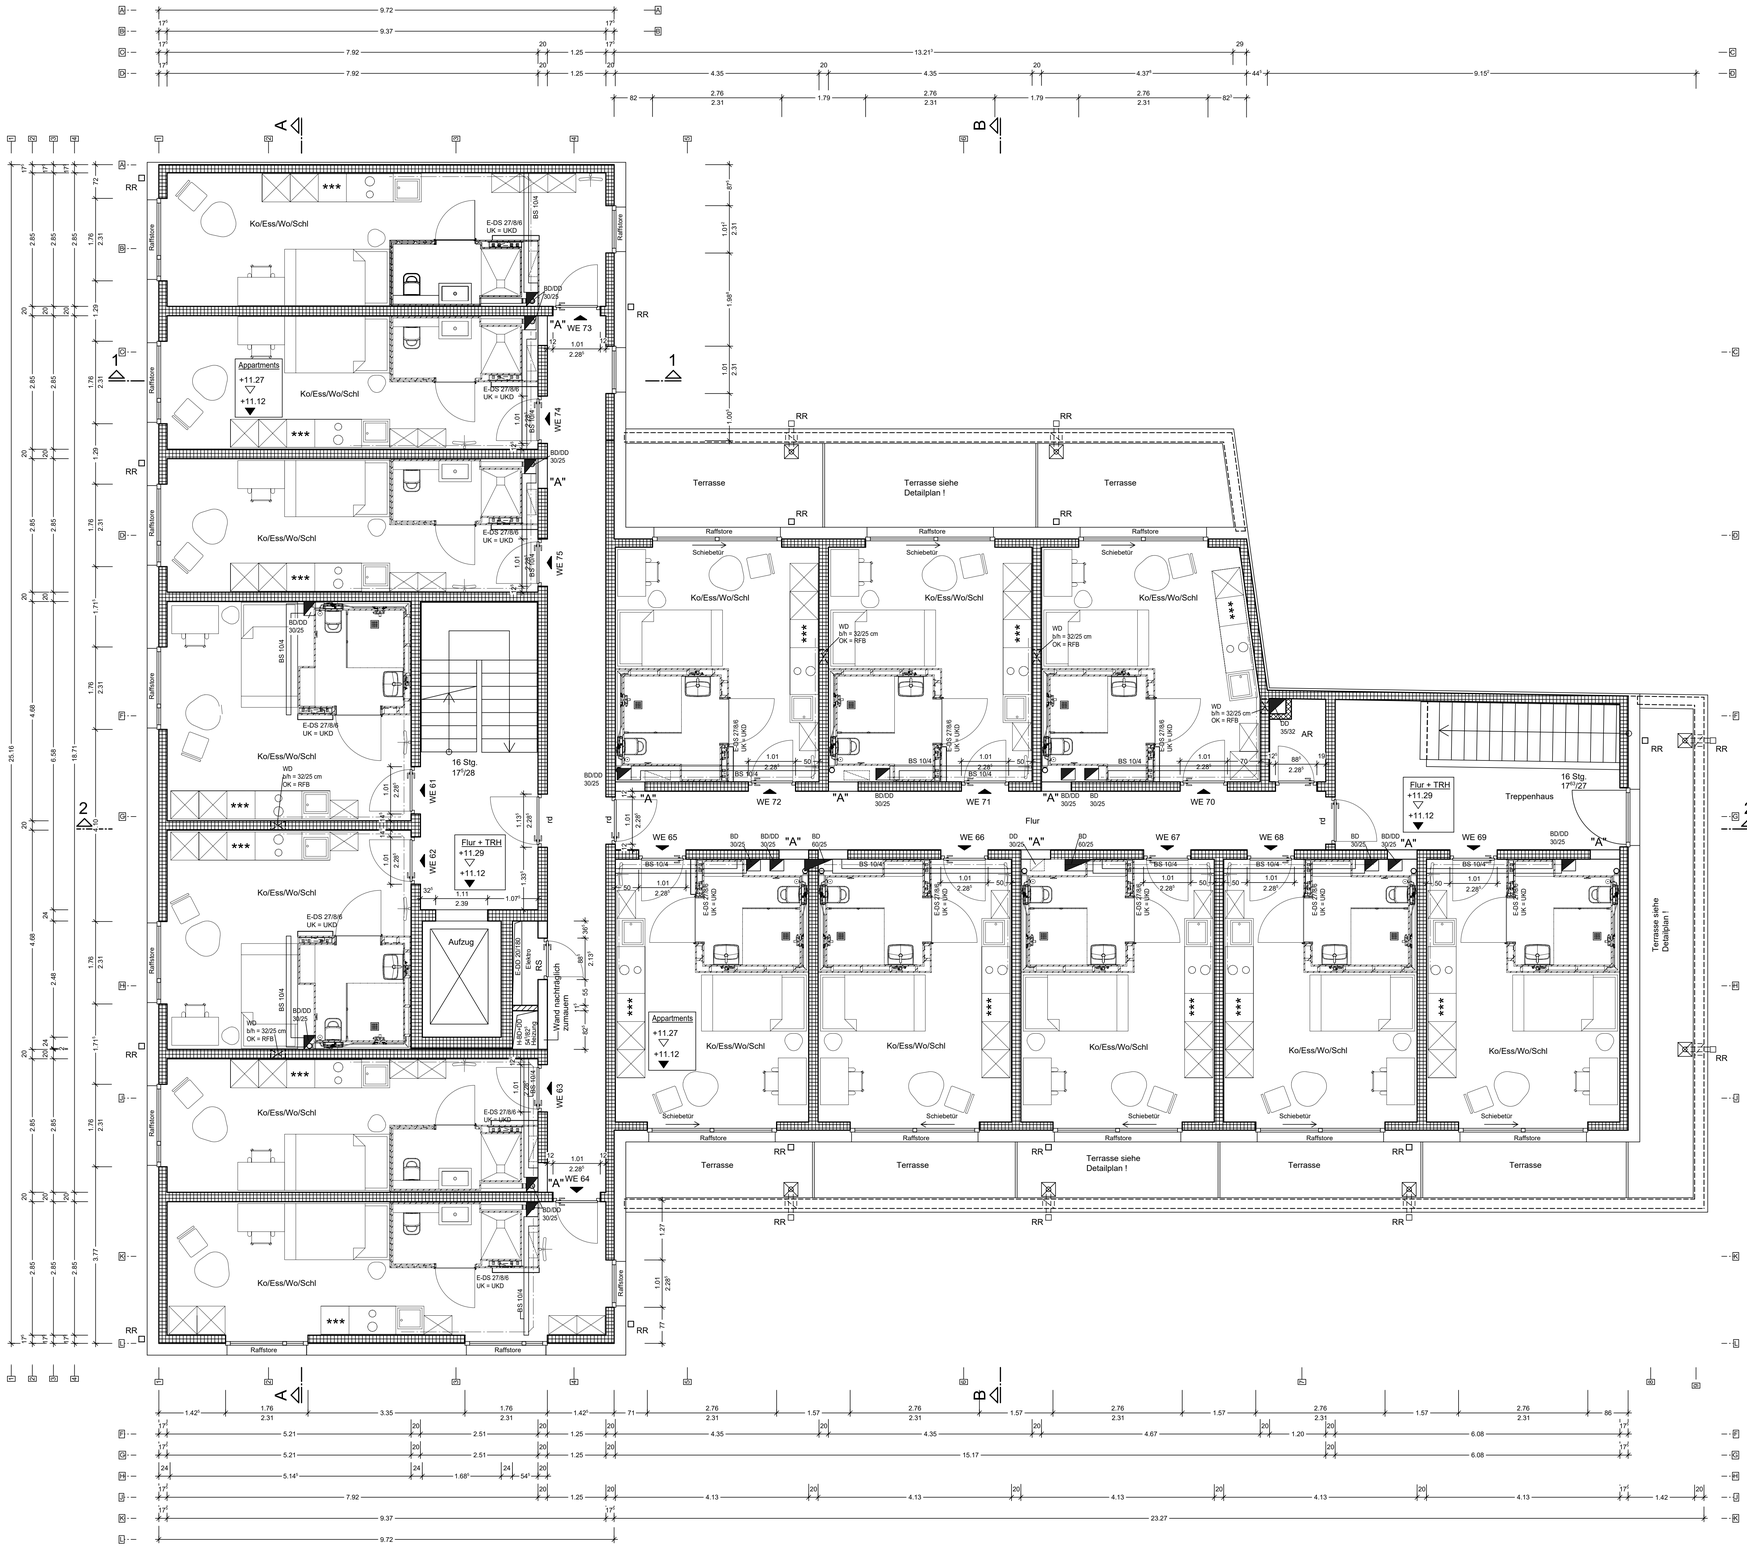


ACHTUNG:
Die zulässige Gesamtabweichung vom Lot der Aufzugsschacht-gesamthöhe von 20mm ist unbedingt einzuhalten!
Die zulässige Maßabweichung (Förderhöhe / Etagenhöhe) beträgt ebenfalls ±20mm (bezogen auf die einzelnen Etagen und auf die Gesamt-höhe). Der Plan der Aufzugs-firma mit Maßen, Einbauteilen, Vorschriften ist zu beachten und auszuführen!

DAS BAUGRUNDGUTACHTEN DES GEOTECHNISCHEN INSTITUTS PROF. DR. GRÜNDER IST ZU BEACHTEN UND EINZUHALTEN!

SÄMTLICHE NICHTTRAGENDEN WÄNDE 1-2 CM ABSTAND ZUR DECKE
NICHTRAGENDE WOHNUNGSTRENNWÄNDE SIND ENTSPRECHEND DEN VORSCHRIFTEN NACH HERSTELLERANGABE AUSZUBILDEN !
DIE ERSTE STEINREIHE (UNTERSTE SCHICHT) IST IN JEDER WAND IM EG (TRAGEND UND NICHTRAGEND) MIT EINEM KS-ISO-KIMMSTEIN ZU MAUERN, FALLS NICHTS ANDERES ANGEGEBEN !

- Stahlbeton
- Kalksplitt Stfkl. 20/2.0/Dünnbettmörtel
- Kalksplitt Stfkl. 12/1.4/Dünnbettmörtel

ALLE TÜR- UND BRÜSTUNGSMASZE AB OKRFB!

SÄMTLICHE AUFZUGSTÜREN VOM KG/TG BIS DG NACH DIN 18090!

24.0 CM WÄRMEDÄMMUNG 0,32 RUNDUM
FALLS NICHTS ANDERES ANGEGEBEN

- VORMAUERUNG 125 CM HOCH
- VORMAUERUNG RAUMHOCH MAUERWERK NACHTRÄGLICH HERSTELLEN! BEI FALLSCHÄCHTEN ROHDICHTE 2.0

- UNTER SÄMTLICHEN NICHTTRAGENDEN WÄNDEN IST IN ALLEN GESCHOSSEN UNTER DER 1. STEINREIHE EIN PAPPSTREIFEN EINZULEGEN!

ACHTUNG:
ALLE TREPPENHAUS-, AUFZUGS- UND WOHNUNGSTRENNWÄNDE IN KS STEINROHDICHTEKLASSE 2.0 (AUSSER BETON)

Fußbodenbeläge:

Raum	Belag
Appartment	Vinylbelag in Holzoptik
Gemeinschaftsräume, Fitnessraum	Vinylbelag in Holzoptik
Bäder, WC's	Feinsteinzeugfliesen
Waschmaschinen, Lager, Heizung, Elektro	Feinsteinzeugfliesen
Müllraum, Fahrradraum	Estrich + Beschichtung
Flure	Teppich
Treppenraum (Hauptpodest)	Teppich
Treppenstufen, Zwischenpodeste	Beton
Technik,	Estrich + Beschichtung

318,65 m NN = ± 0,00 m

SÄMTLICH MASZE SIND AM BAU ZU PRÜFEN, ALLE BAUTEILE NACH STATIK

Vorabzug
Stand 23.09.2026

Werkplan 4. OG

NEUBAU EINES STUDENTENWOHNHEIMES
MARTIN-RICHTER-STRASSE 17
90489 NÜRNBERG

BAUHERR:
SIEBENTRITT & DONAUER GMBH
KORNSTRASSE 108
92318 NEUMARKT

ENTWURF:

PLANUNG:

INGENIEURBÜRO STOCKHECKE
BAUSTATIK BAUKONSTRUKTION PLANUNG BAUPHYSIK
Randstraße 1 90552 Röthenbach
T 0911 57 68 00 F 0911 9 50 26 83
info@baustatik-stockhecke.de

WERKPLAN 4. OBERGESCHOSS

M 1 : 50

PLAN 5

RÖTHENBACH, im Mai 2026