Schnitt A-A

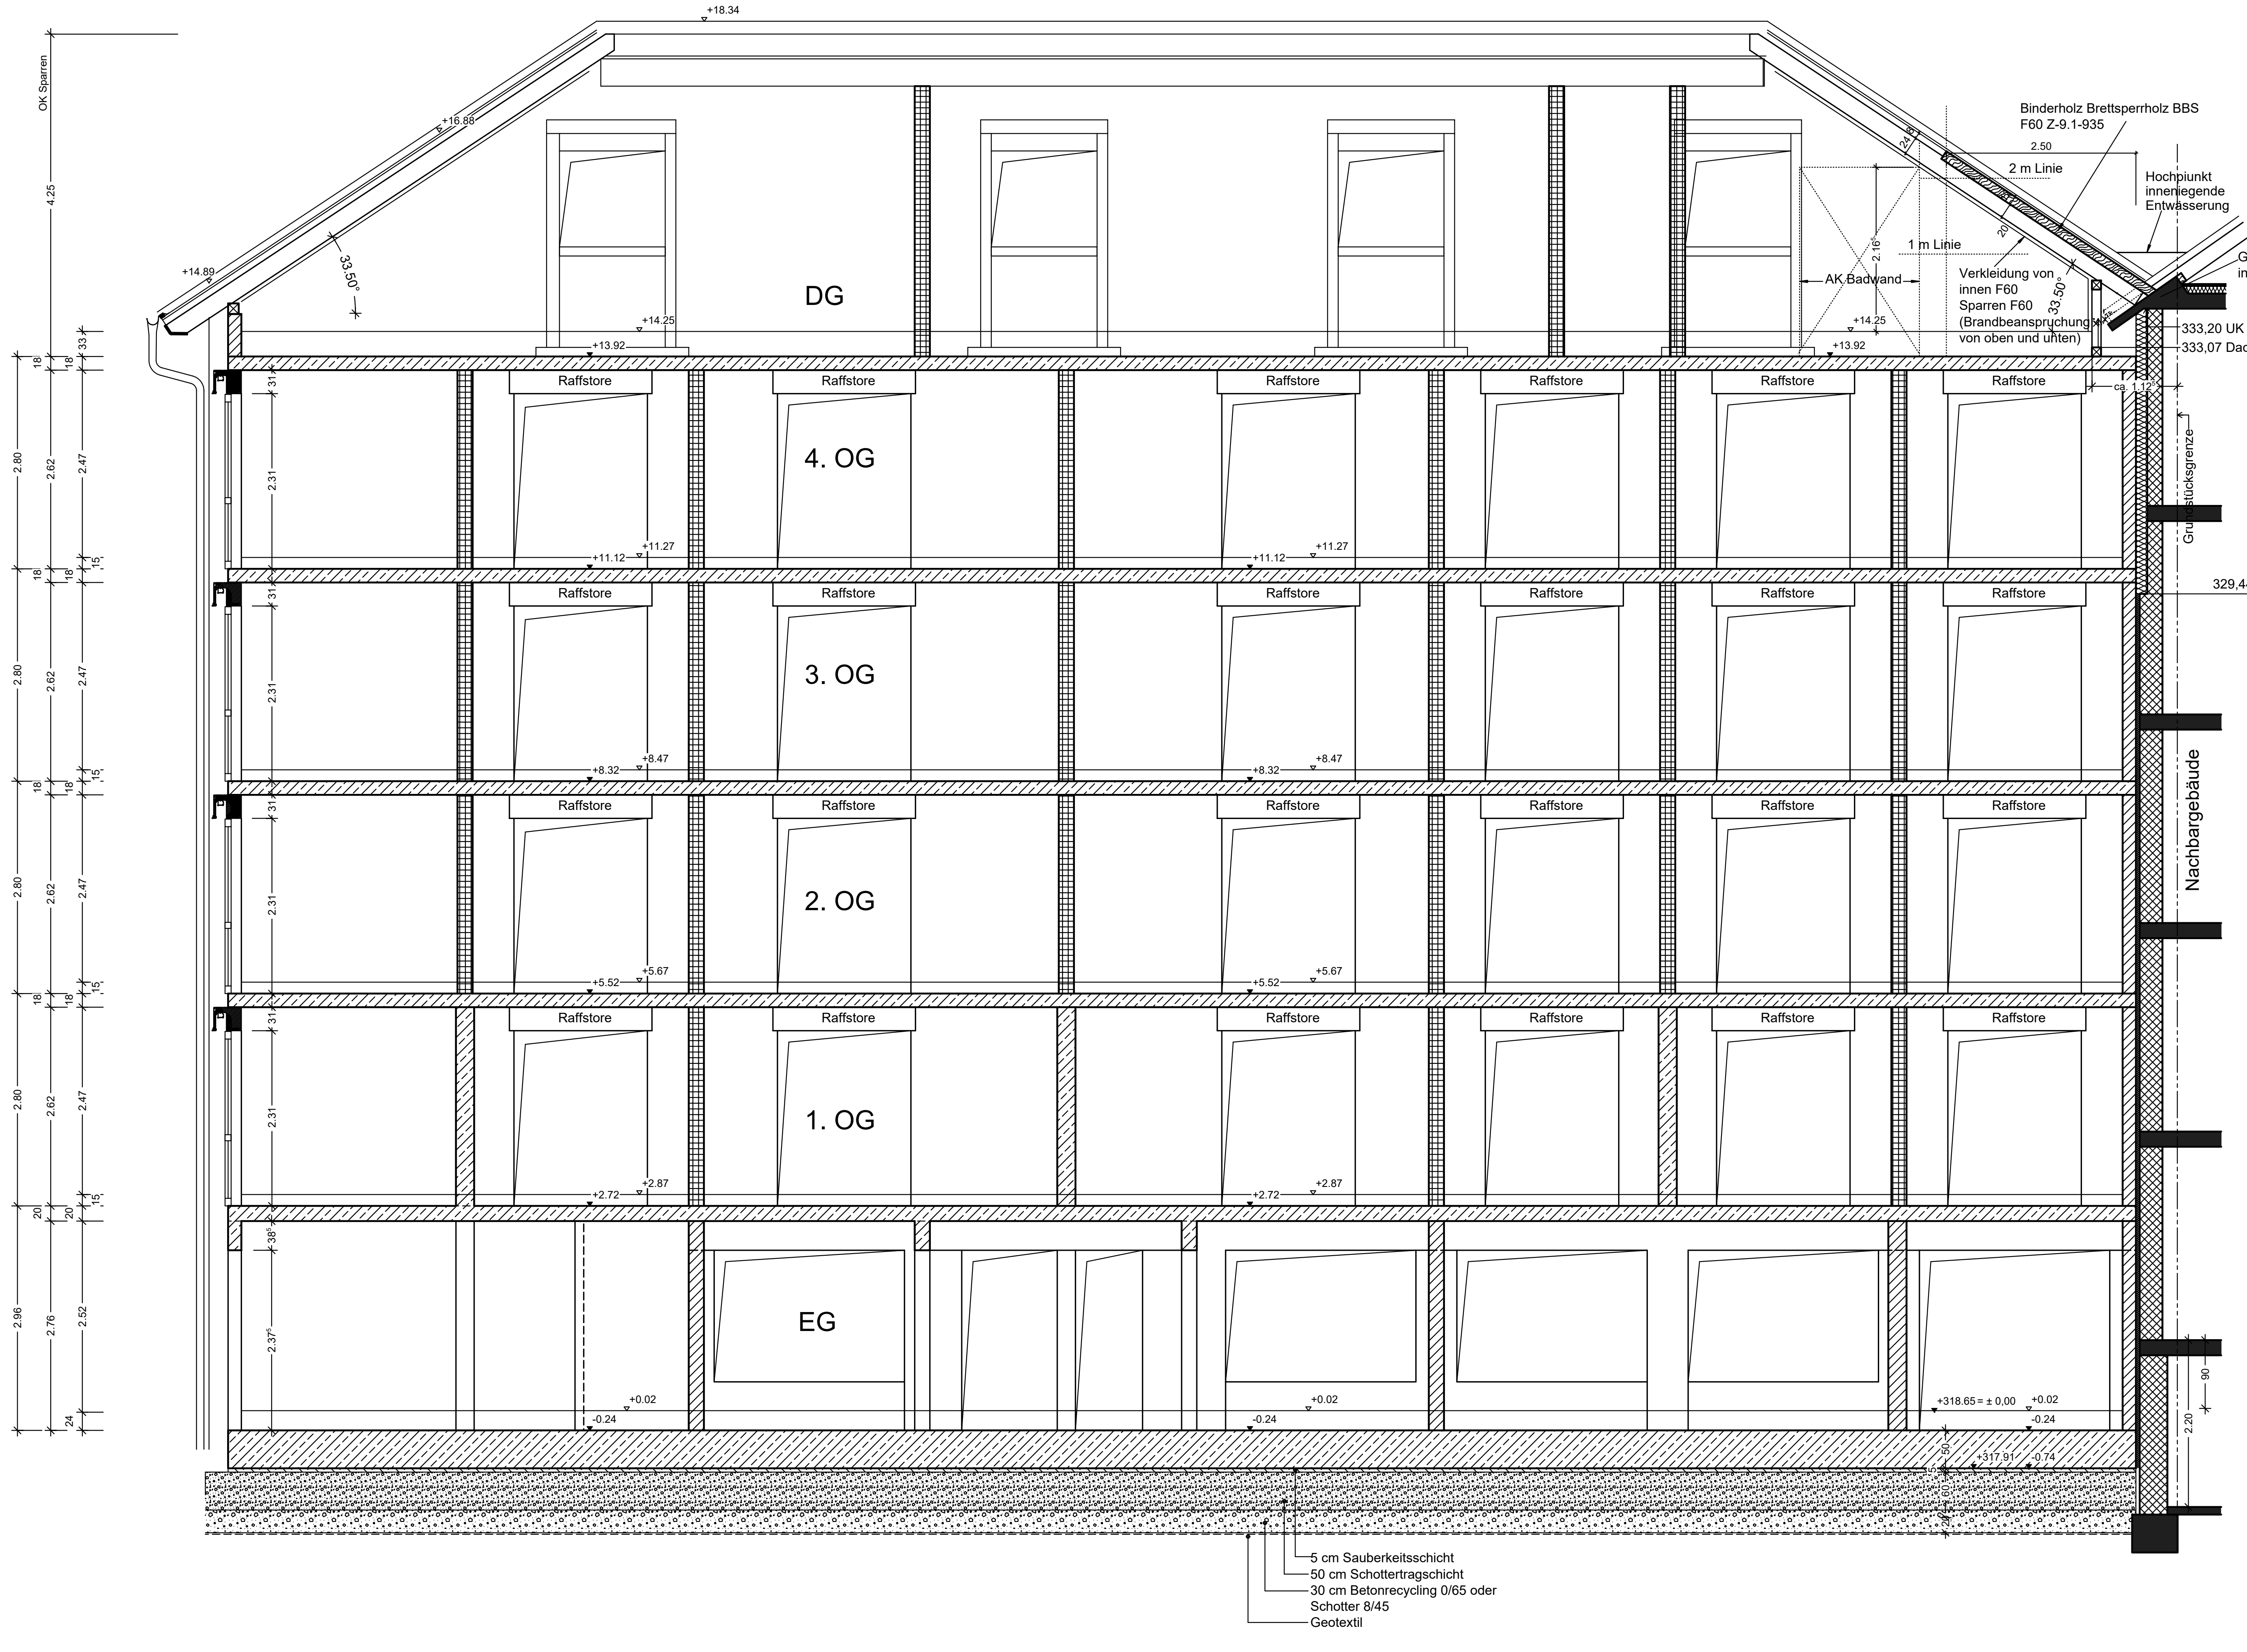

Schnitt B-B

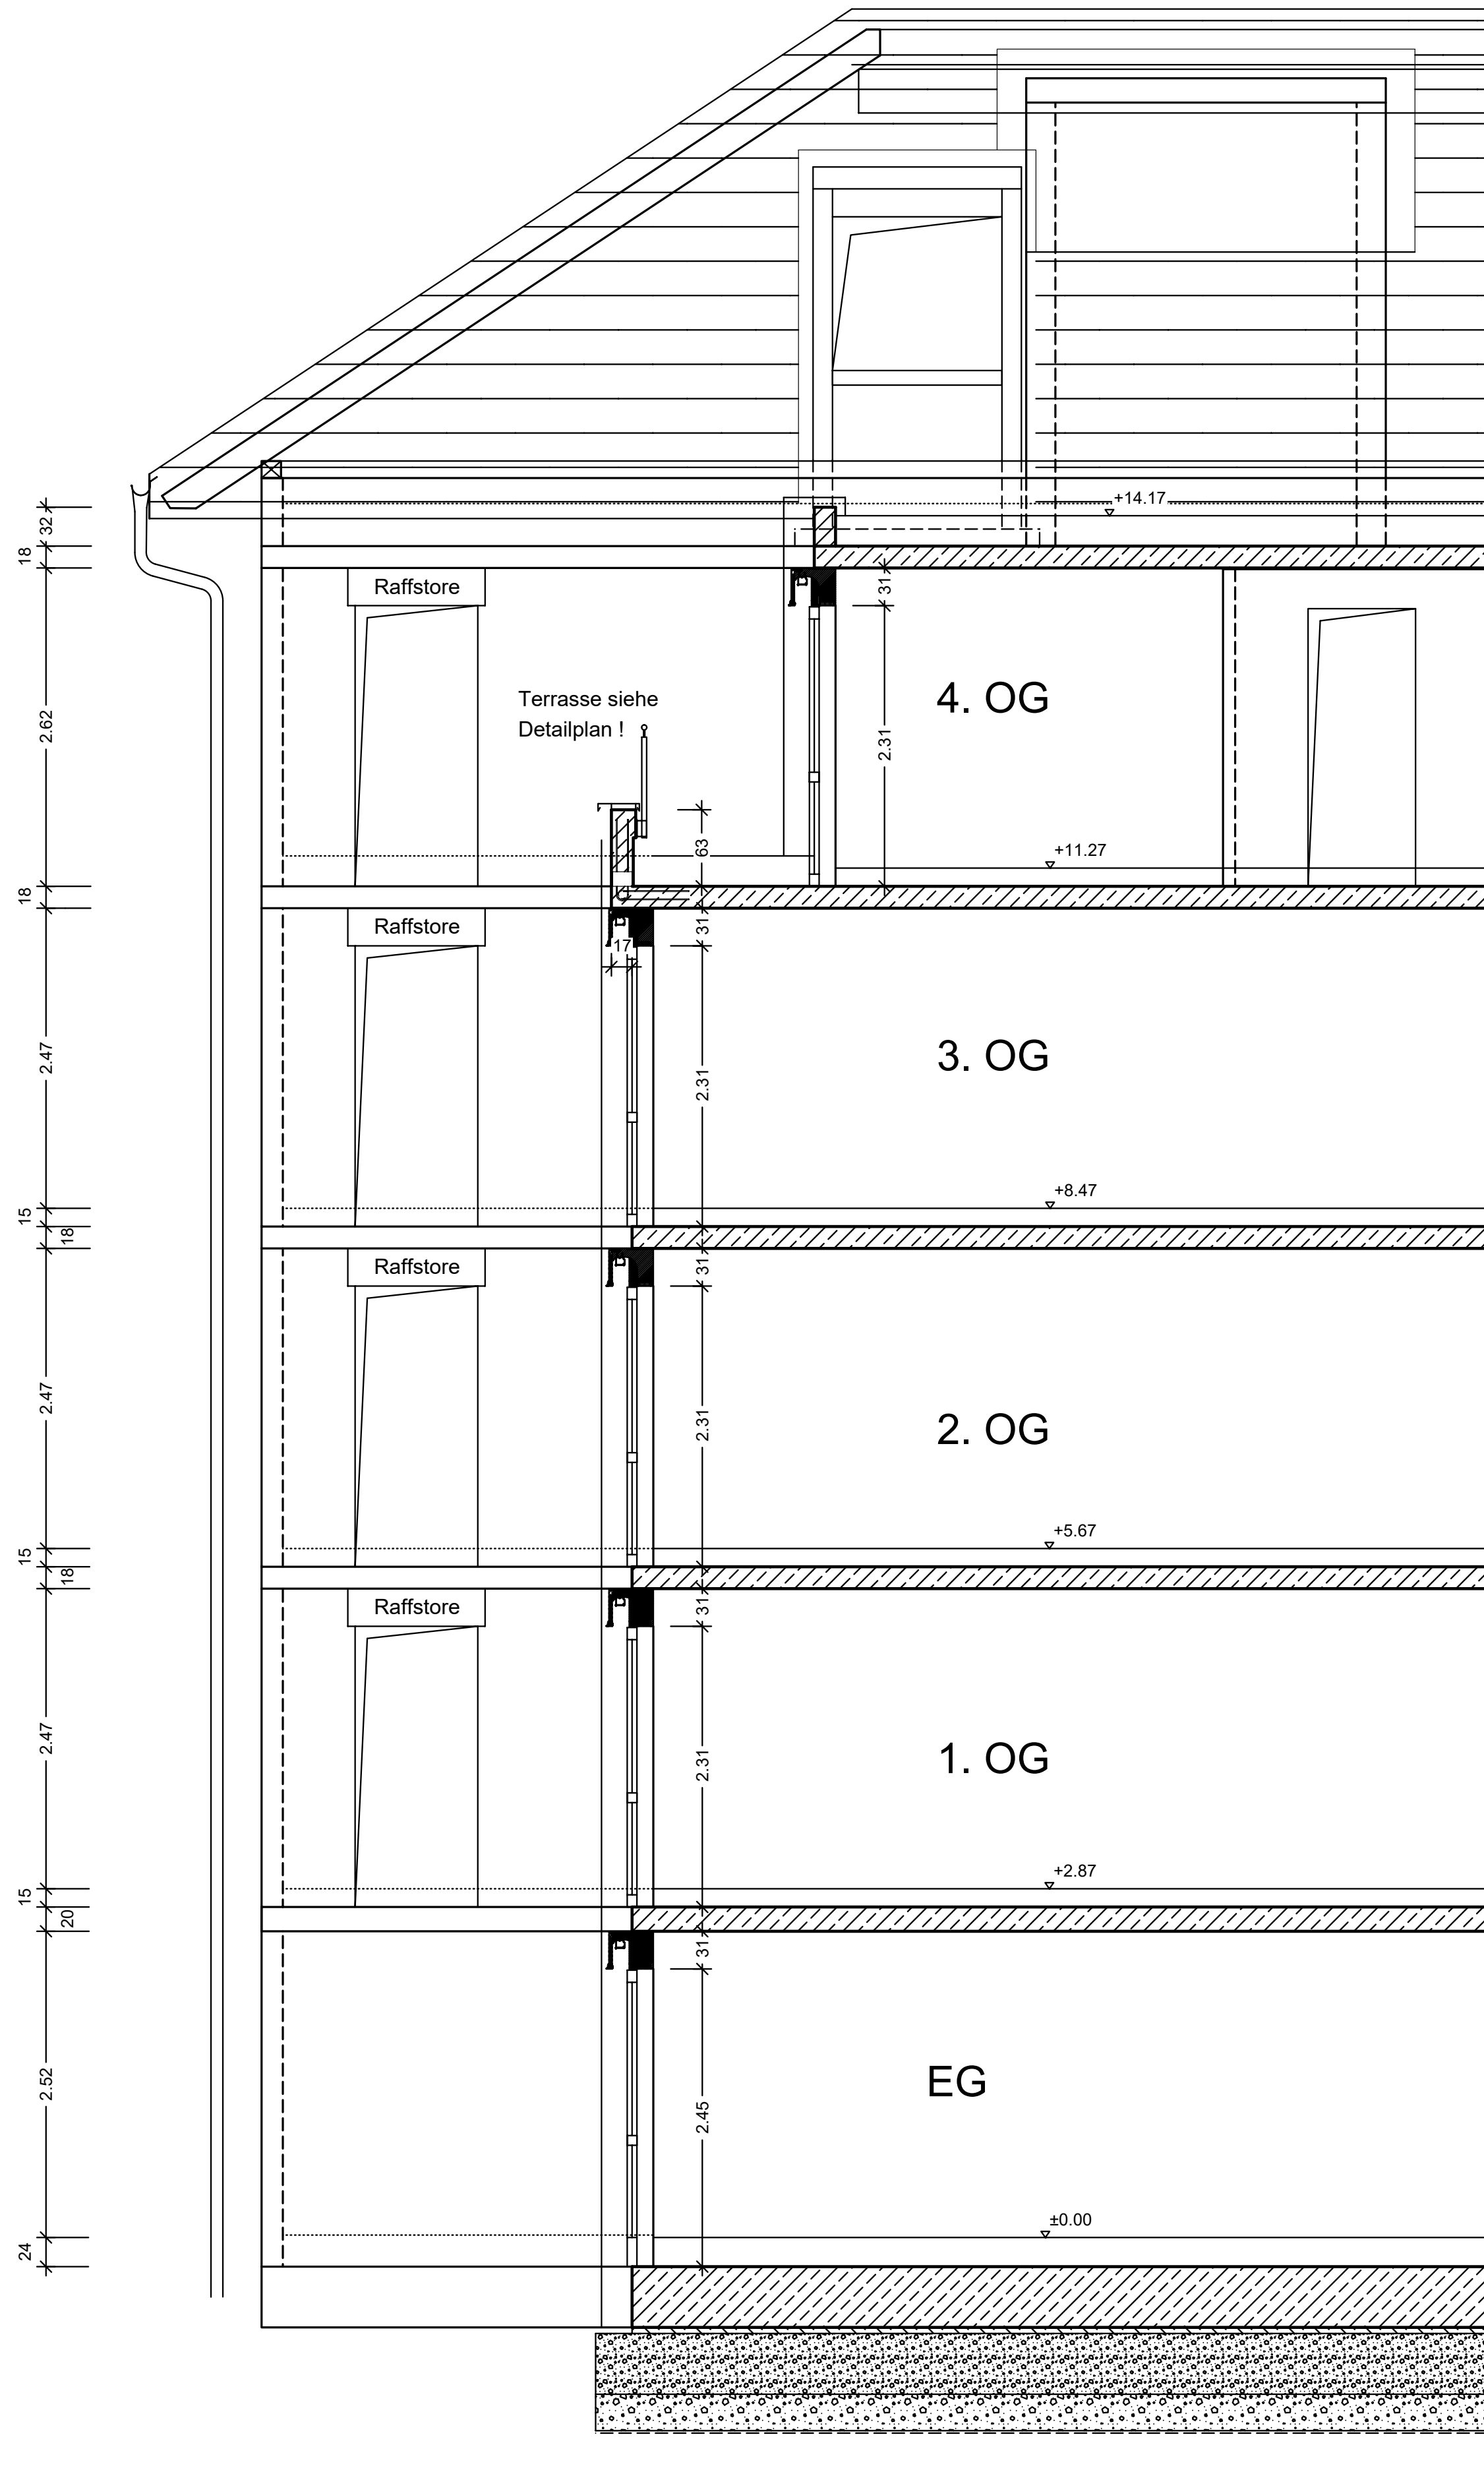

ACHTUNG:

Die zulässige Gesamtabweichung vom Lot der Aufzugsschachtgesamthöhe von 20mm ist unbedingt einzuhalten!
Die zulässige Maßabweichung (Förderhöhe / Etagenhöhe) beträgt ebenfalls ±20mm (bezogen auf die einzelnen Etagen und auf die Gesamthöhe). Der Plan der Aufzugsfirma mit Maßen, Einbauteilen, Vorschriften ist zu beachten und auszuführen!

DAS BAUGRUNDGUTACHTEN DES GEOTECHNISCHEN INSTITUTS PROF. DR. GRÜNDER IST ZU BEACHTEN UND EINZUHALTEN!

SÄMTLICHE NICHTTRAGENDEN WÄNDE 1-2 CM ABSTAND ZUR DECKE
NICHTRAGENDE WOHNUNGSTRENNWÄNDE SIND ENTSPRECHEND DEN VORSCHRIFTEN NACH HERSTELLERANGABE AUSZUBILDEN !
DIE ERSTE STEINREIHE (UNTERSTE SCHICHT) IST IN JEDER WAND IM EG (TRAGEND UND NICHTRAGEND) MIT EINEM KS-ISO-KIMMSTEIN ZU MAUERN, FALLS NICHTS ANDERES ANGEGEBEN !

▨ Stahlbeton
▦ Kalksplitt Stfkl. 20/2.0/Dünnbettmörtel
▨ Kalksplitt Stfkl. 12/1.4/Dünnbettmörtel

ALLE TÜR- UND BRÜSTUNGSMASZE AB OKRFB!

SÄMTLICHE AUFZUGSTÜREN VOM EG BIS DG NACH DIN 18090!

24.0 CM WÄRMEDÄMMUNG 0,32 RUNDUM
FALLS NICHTS ANDERES ANGEGEBEN

▨ VORMAUERUNG 125 CM HOCH

▩ VORMAUERUNG RAUMHOCH
MAUERWERK NACHTRÄGLICH HERSTELLEN!
BEI FALLSCHÄCHTEN ROHDICHTE 2.0

- UNTER SÄMTLICHEN NICHTRRAGENDEN WÄNDEN IST IN ALLEN GESCHOSSEN UNTER DER 1. STEINREIHE EIN PAPPSTREIFEN EINZULEGEN!

ACHTUNG:
ALLE TREPPENHAUS-, AUFZUGS- UND WOHNUNGSTRENNWÄNDE IN KS STEINROHDICHTEKLASSE 2.0 (AUSSER BETON)

Fußbodenbeläge:

Raum	Belag
Appartment	Vinylbelag in Holzoptik
Gemeinschaftsräume, Fitnessraum	Vinylbelag in Holzoptik
Bäder, WC's	Feinsteinzeugfliesen
Waschmaschinen, Lager, Heizung, Elektro	Feinsteinzeugfliesen
Müllraum, Fahrradraum	Estrich + Beschichtung
Flure	Teppich
Treppenraum (Hauptpodest)	Teppich
Treppenstufen, Zwischenpodeste	Beton
Technik,	Estrich + Beschichtung

318,65 m NN = ± 0,00 m

SÄMTLICH MASZE SIND AM BAU ZU PRÜFEN, ALLE BAUTEILE NACH STATIK

Vorabzug
Stand 23.09.2026

Werkplan Schnitte A/B

NEUBAU EINES STUDENTENWOHNHEIMES
MARTIN-RICHTER-STRASSE 17
90489 NÜRNBERG

BAUHERR:
SIEBENTRITT & DONAUER GMBH
KORNSTRASSE 108
92318 NEUMARKT

ENTWURF:
ARCHITEKTURBÜRO HAUSBLAU, ROBERT RESCH
KUCHA 302 IN 91238 OFFENHAUSEN
TEL: 09158/998979

PLANUNG:

INGENIEURBÜRO
STOCKHECKE
BAUSTATIK BAUKONSTRUKTION PLANUNG BAUPHYSIK
Randstraße 1 90552 Röthenbach
T 0911 57 68 00 F 0911 9 50 26 83
info@baustatik-stockhecke.de

WERKPLAN SCHNITTE A-A, B-B

M 1 : 50

PLAN 8

RÖTHENBACH, im Mai 2026

H/B = 650 / 1440 (0.94m²)
Allplan 2025